


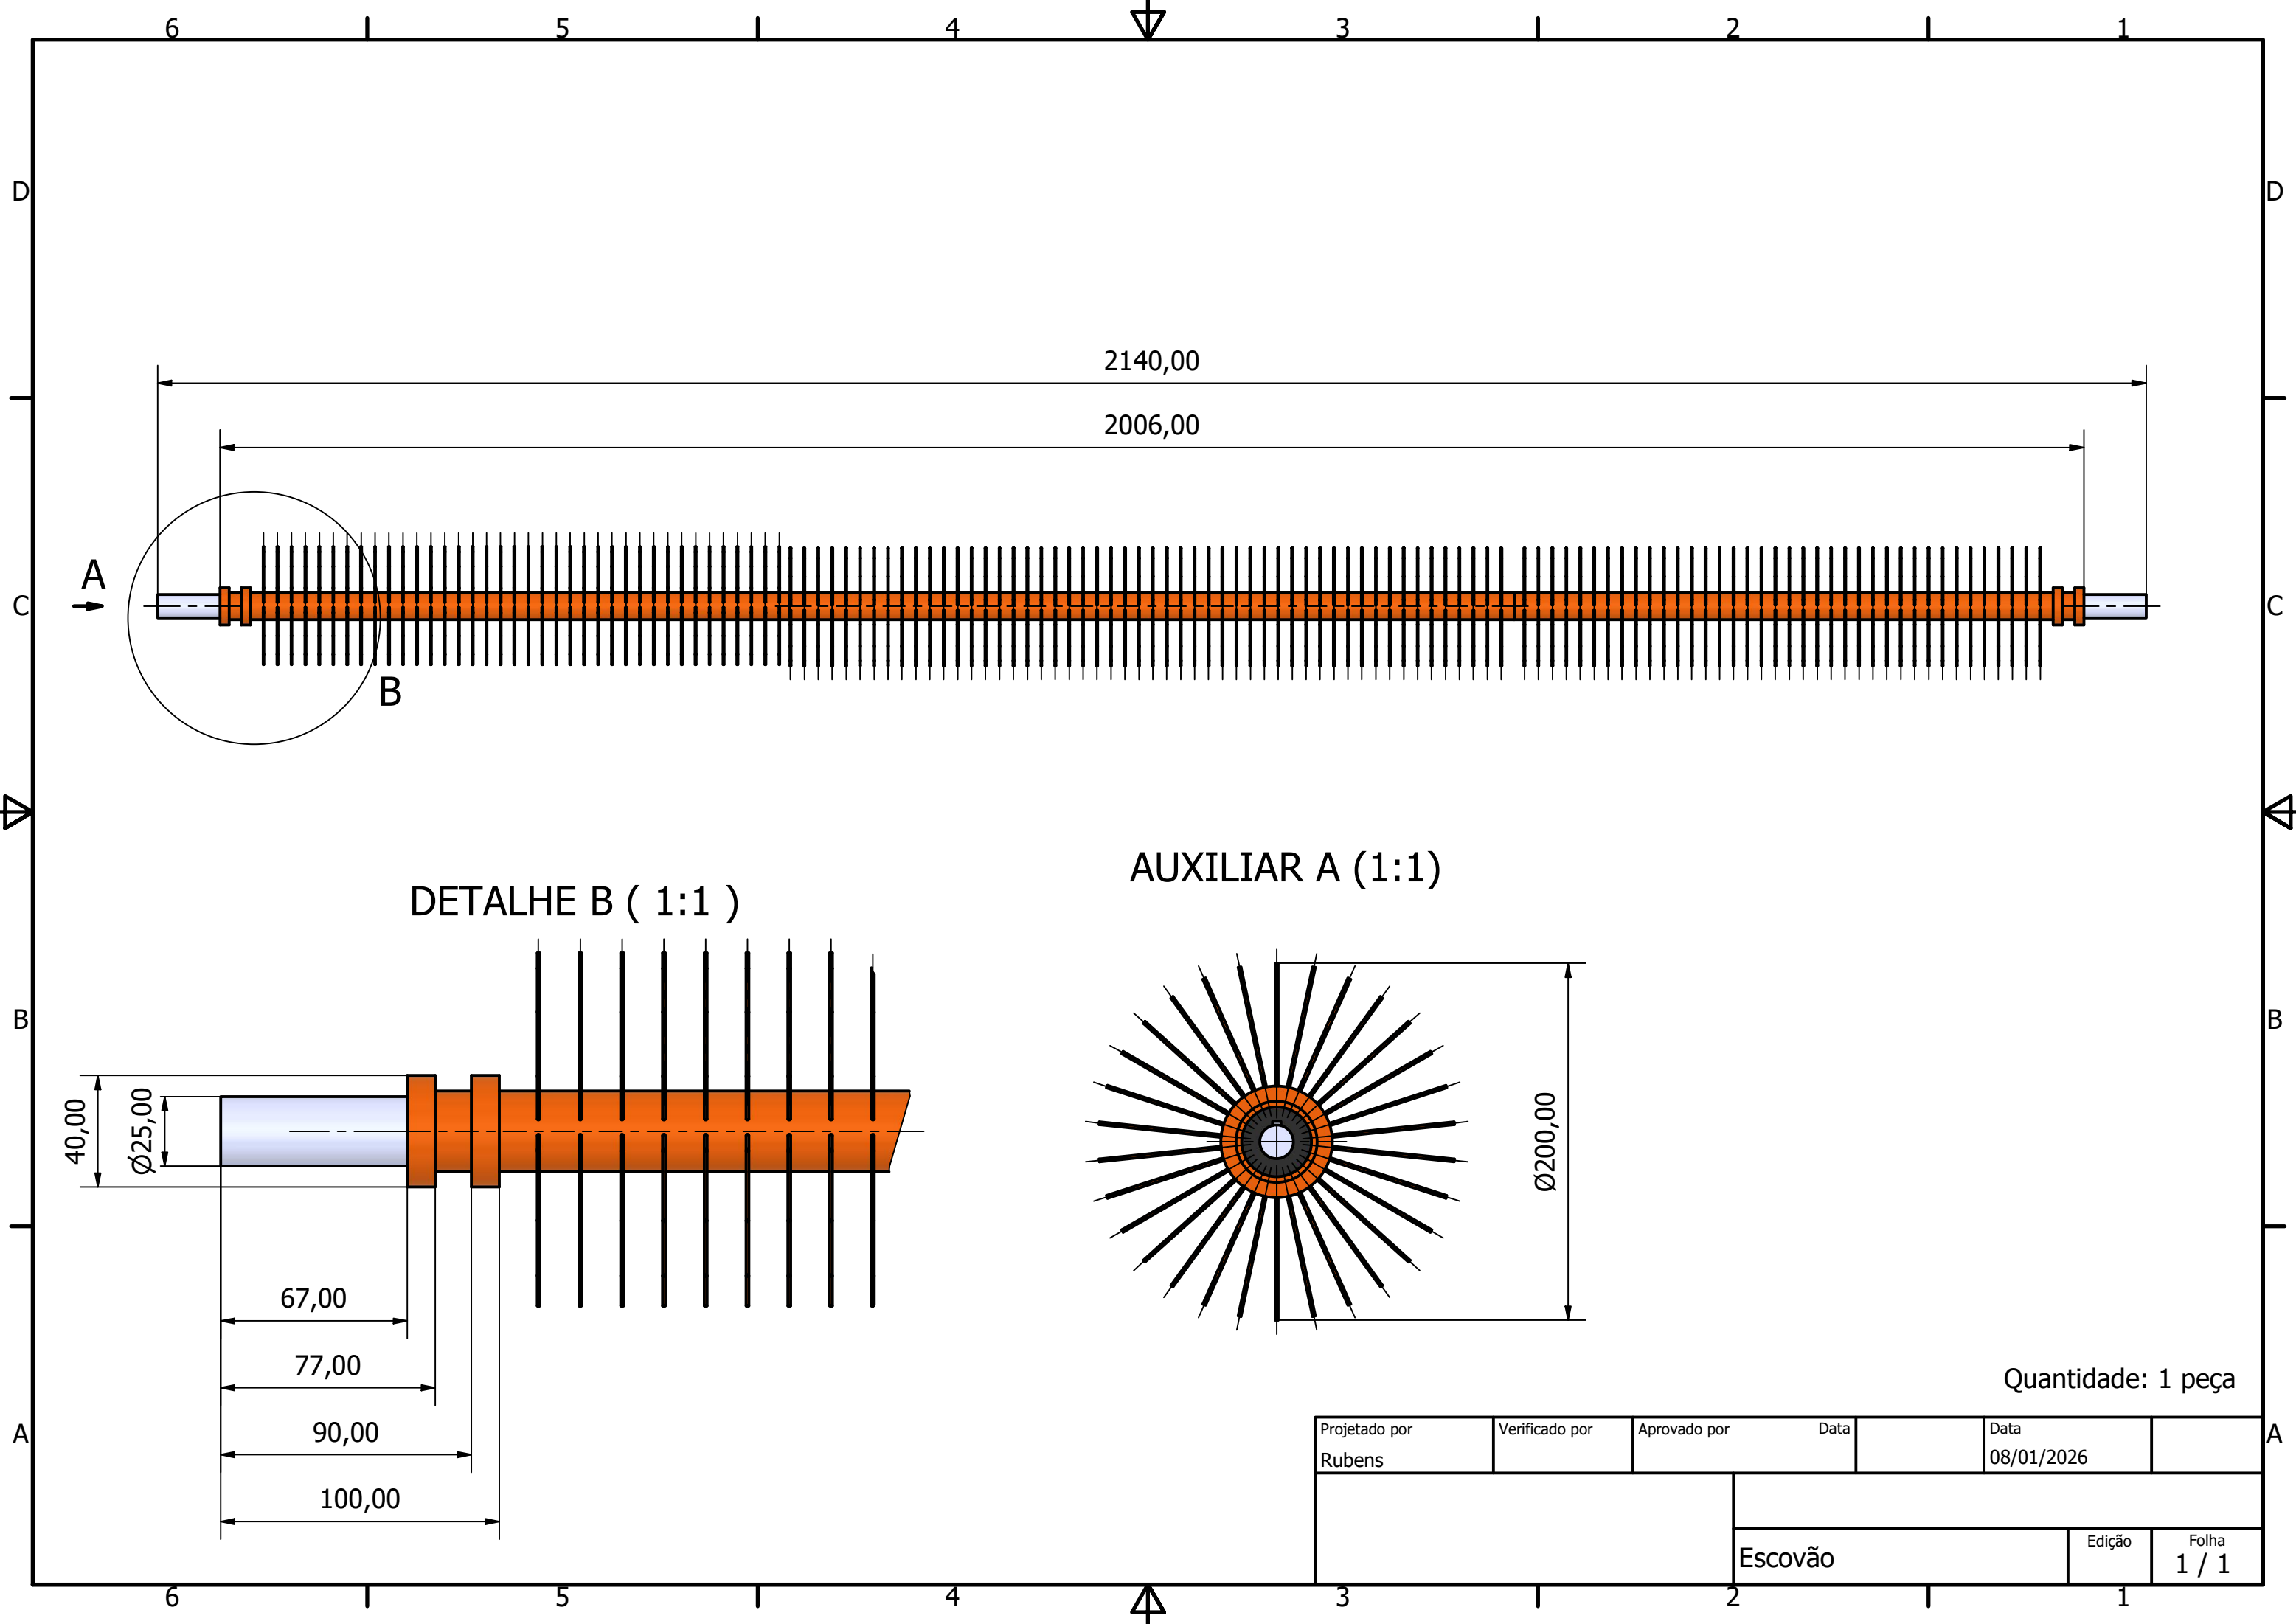

Quantidade: 1 peça

Projetado por Rubens	Verificado por	Aprovado por	Data		Data 08/01/2026	
			Escovão			
			Edição		Folha 1 / 1	