


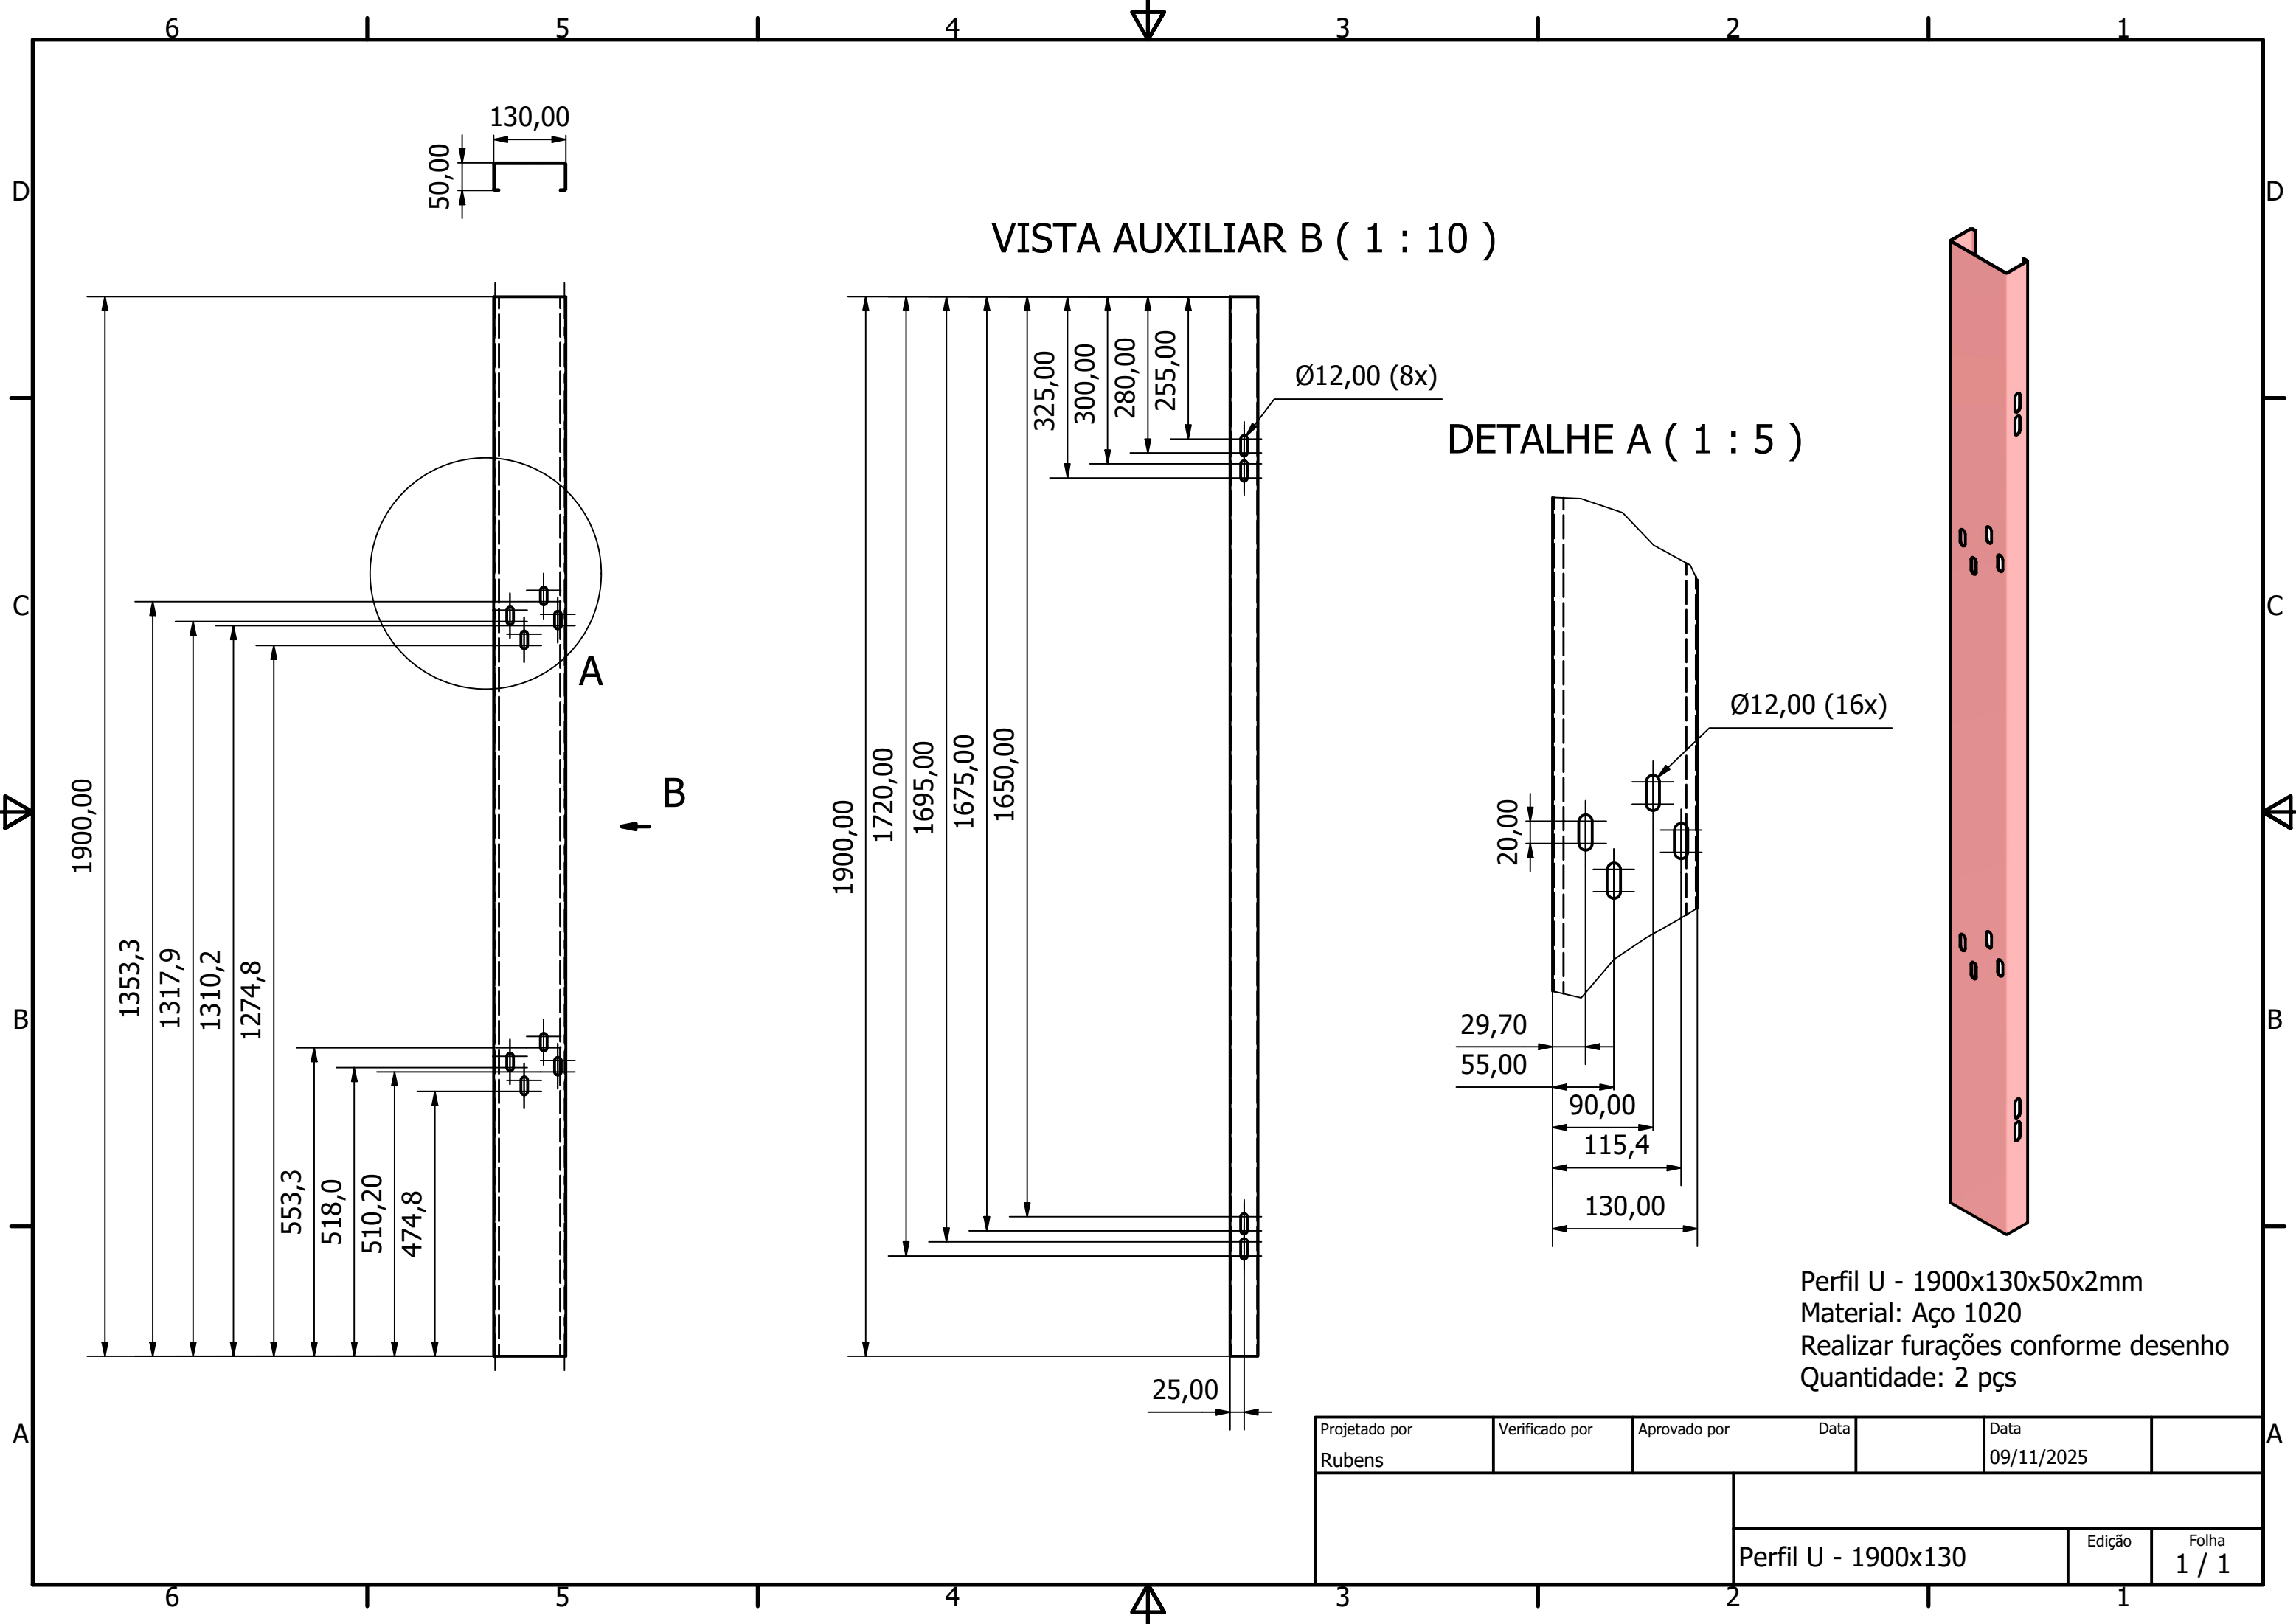

VISTA AUXILIAR B (1 : 10)

DETALHE A (1 : 5)

Perfil U - 1900x130x50x2mm
Material: Aço 1020
Realizar furações conforme desenho
Quantidade: 2 pçs

Projetado por Rubens	Verificado por	Aprovado por	Data 09/11/2025	
		Perfil U - 1900x130		
		Edição	Folha 1 / 1	